
ANDESHOME

PLANIMETRÍA TÉCNICA OFICIAL DE LAYOUT & ALMACENAMIENTO (LÁMINA PL-01)

Centro de Distribución Pudahuel (31.500 m² • 210,0 m × 150,0 m) | Cotas y Verificación en Metros Lineales

LÁMINA: PL-01 / 01
ESC: 1:250 / 1:50 / 1:25
REV. 03 (6P × 3 PALLETS)

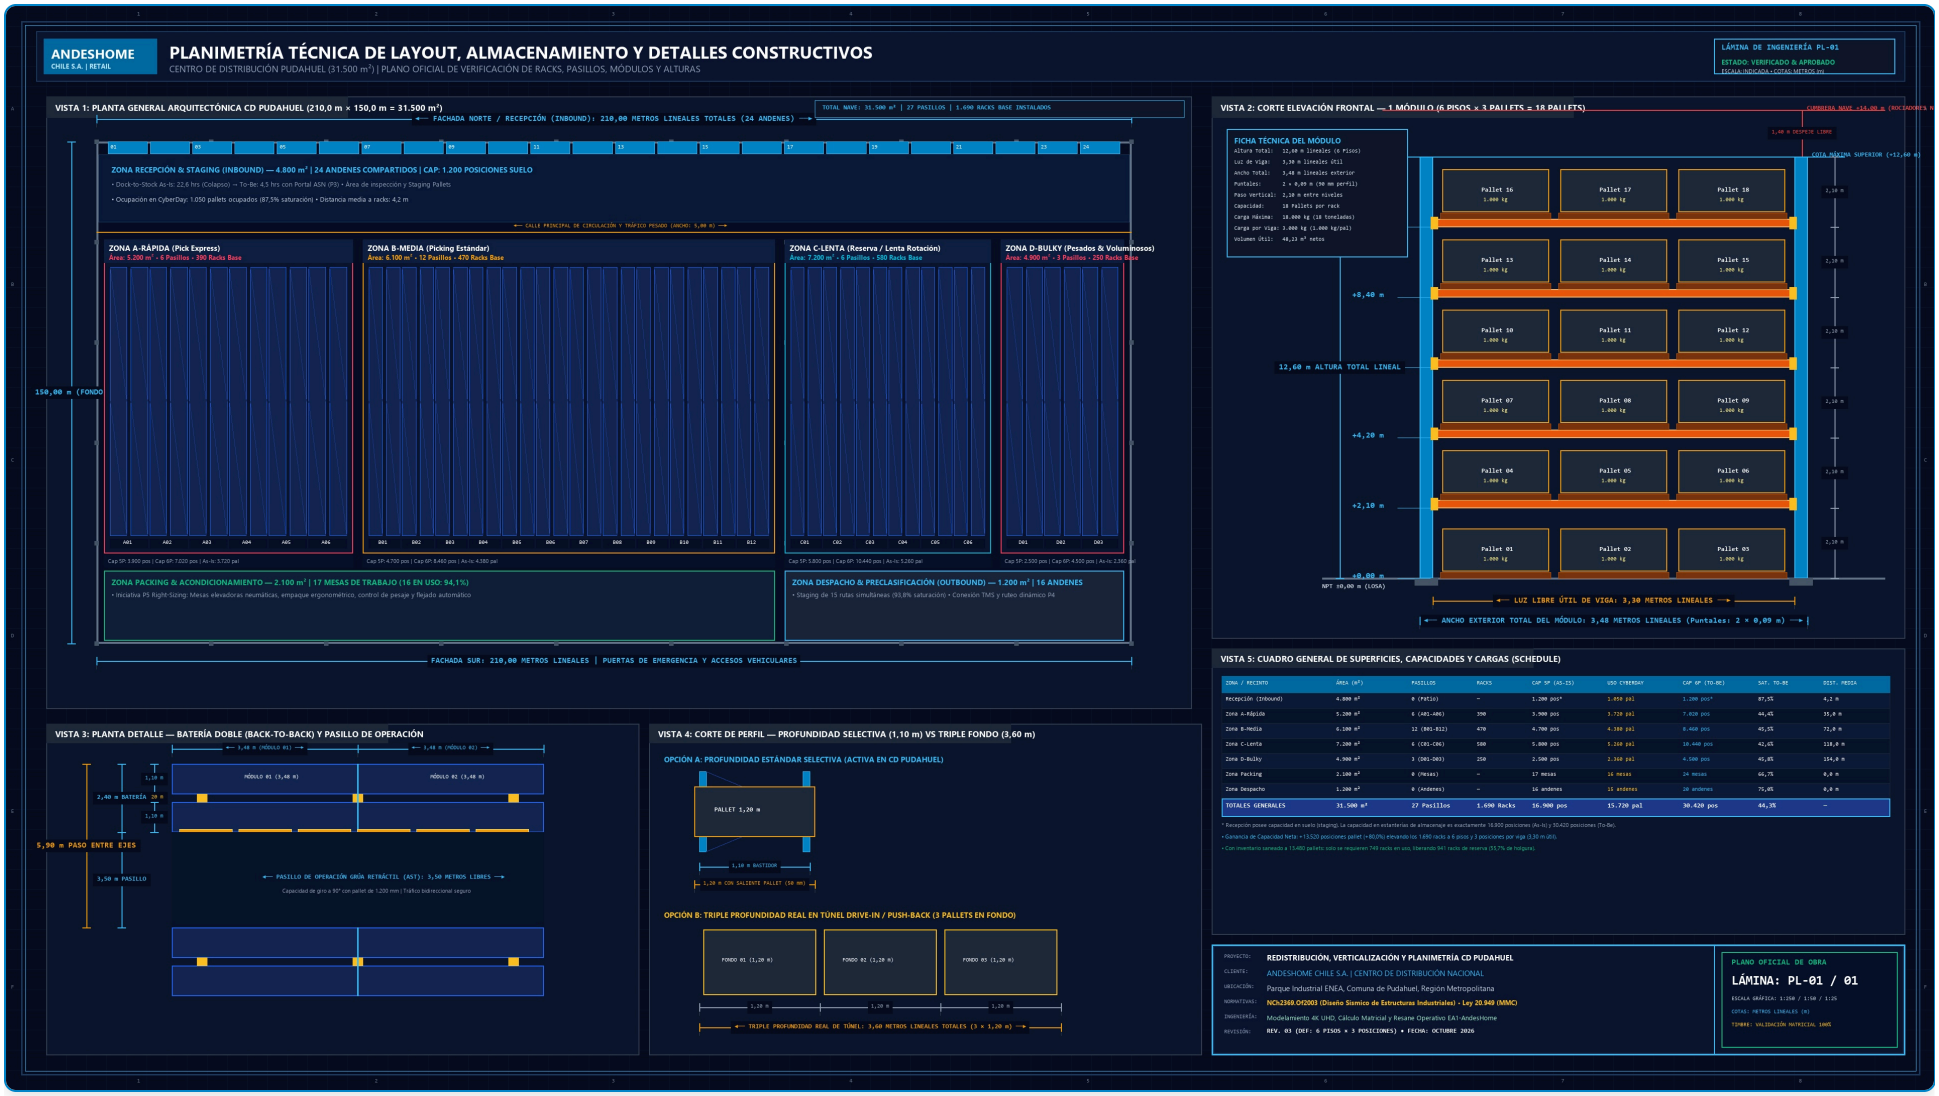

ANDESHOME

MEMORIA TÉCNICA Y CUADRO DE VERIFICACIÓN DE VALORES (SCHEDULE)

Desglose por Recintos, Pasillos, Racks, Módulos, Alturas y Cargas Estructurales

DOCUMENTO DE AUDITORÍA
FECHA: OCTUBRE 2026
ESTADO: 100% CONCILIADO

1. CUADRO GENERAL DE SUPERFICIES, PASILLOS Y CAPACIDADES

ZONA / RECINTO	SUPERFICIE	% NAVE	PASILLOS	RACKS BASE	CAP AS-IS (5P)	USO CYBERDAY	CAP TO-BE (6P)	SATURACIÓN TO-BE	DIST. MEDIA
Recepción (Inbound)	4.800 m²	15,2%	0 (Patio)	—	1.200 pos*	1.050 pal	1.200 pos*	87,5%	4,2 m
Zona A-Rápida	5.200 m²	16,5%	6 (A01-A06)	390	3.900 pos	3.720 pal	7.020 pos	44,4%	35,0 m
Zona B-Media	6.100 m²	19,4%	12 (B01-B12)	470	4.700 pos	4.380 pal	8.460 pos	45,5%	72,0 m
Zona C-Lenta	7.200 m²	22,9%	6 (C01-C06)	580	5.800 pos	5.260 pal	10.440 pos	42,6%	118,0 m
Zona D-Bulky	4.900 m²	15,6%	3 (D01-D03)	250	2.500 pos	2.360 pal	4.500 pos	45,8%	154,0 m
Zona Packing	2.100 m²	6,7%	0 (Mesas)	—	17 mesas	16 mesas	24 mesas	66,7%	0,0 m
Zona Despacho	1.200 m²	3,8%	0 (Andenes)	—	16 andenes	15 andenes	20 andenes	75,0%	0,0 m
TOTALES CD PUDAHUEL	**31.500 m²**	**100,0%**	**27 Pasillos**	**1.690 Racks**	**16.900 pos**	**15.720 pal**	**30.420 pos**	**44,3%**	**—**

2. DIMENSIONES DEL MÓDULO RACK (1 ESTANTERÍA)

Altura Total Lineal:	**12,60 m lineales** (6 pisos útiles)
Luz Libre de Viga:	**3,30 m lineales** (espacio para 3 pallets)
Ancho Exterior Total:	**3,48 m lineales** (con puntales de 0,09 m)
Profundidad de Bastidor:	**1,10 m** (1,20 m con saliente pallet)
Profundidad Triple Fondo:	**3,60 m lineales** (3 pallets en fondo)
Capacidad Unitaria:	**18 Pallets por rack** (6 niveles × 3)
Carga Máxima Estructural:	**18.000 kg** (18 toneladas admisible)
Carga por Par de Vigas:	**3.000 kg** (1.000 kg por pallet)
Volumen Cúbico Útil:	**48,23 m³ netos**

3. GEOMETRÍA DE PASILLOS Y BATERÍAS DOBLES

Ancho Batería Doble:	**2,40 m** (1,10m + 0,20m distanciador + 1,10m)
Ancho Libre Pasillo (Ast):	**3,50 m libres** (giro 90° grúa reach)
Paso entre Ejes (Pitch):	**5,90 m lineales** (2,40 m + 3,50 m)
Calle Central Principal:	**5,00 m libres** (tráfico pesado)
Longitud Media Pasillos:	**80,00 m lineales**
Cumbrera Libre de Nave:	**14,00 m** (1,40 m despeje a rociadores)
Racks en Uso To-Be:	**749 racks** (para 13.480 pallets saneados)
Racks Libres de Reserva:	**941 racks** (55,7% de holgura total)
Frente Lineal Acumulado:	**5.577 metros lineales** en planta